


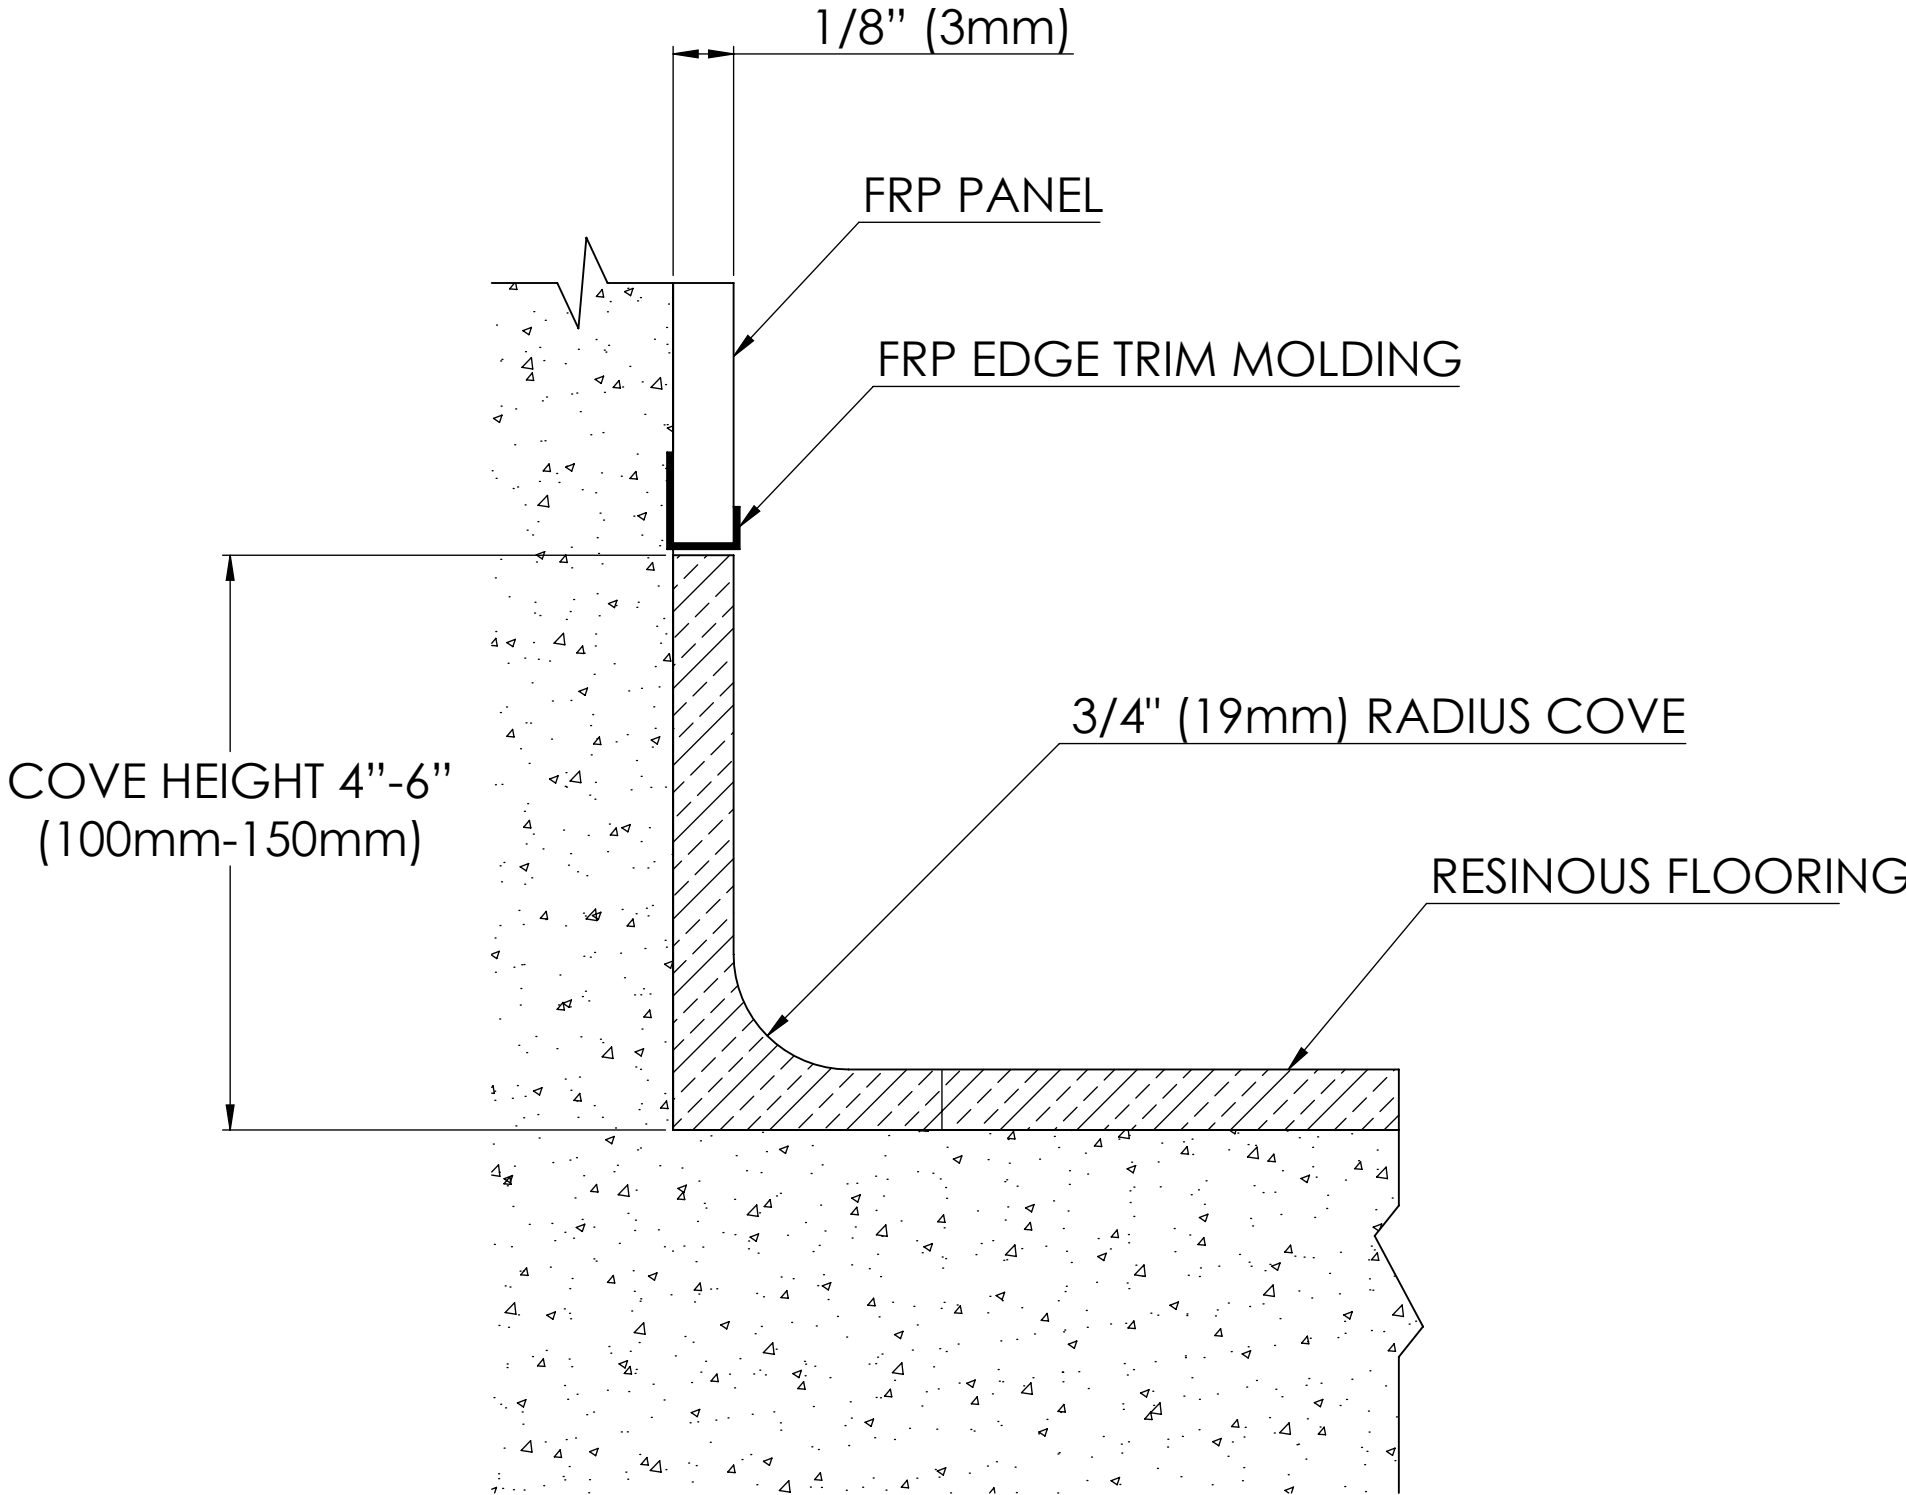

elite crete systems
ENGINEERED HIGH PERFORMANCE SURFACES & FLOORING
www.elitecrete.com
219-465-7671

TITLE		RESINOUS FLOORING FRP WALL PANEL COVE	
DATE		SCALE	AS NOTED
DWG NO.		PROJECT	